




Concrete floor

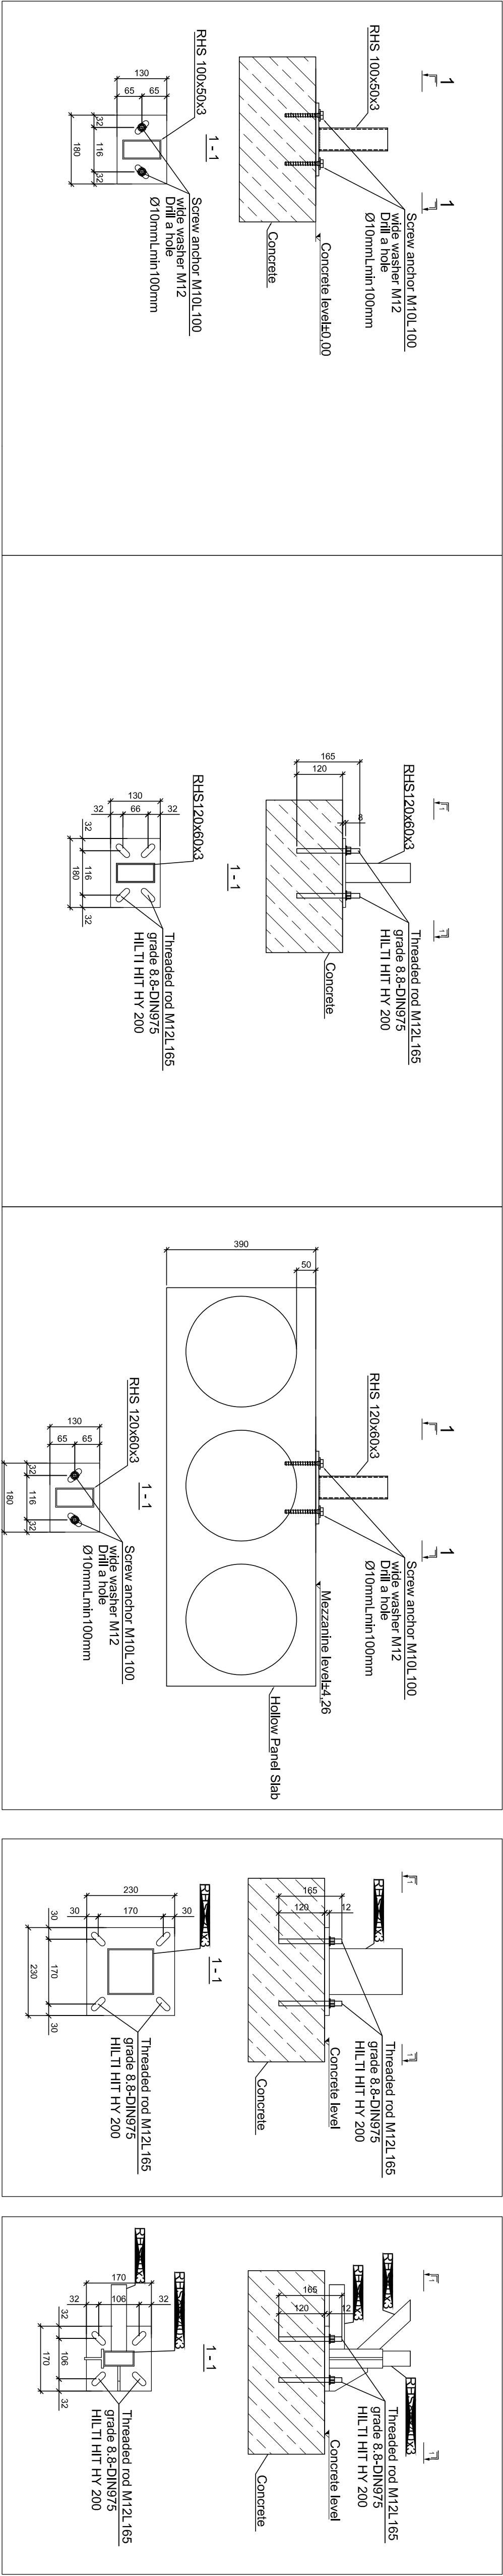


Concrete wall

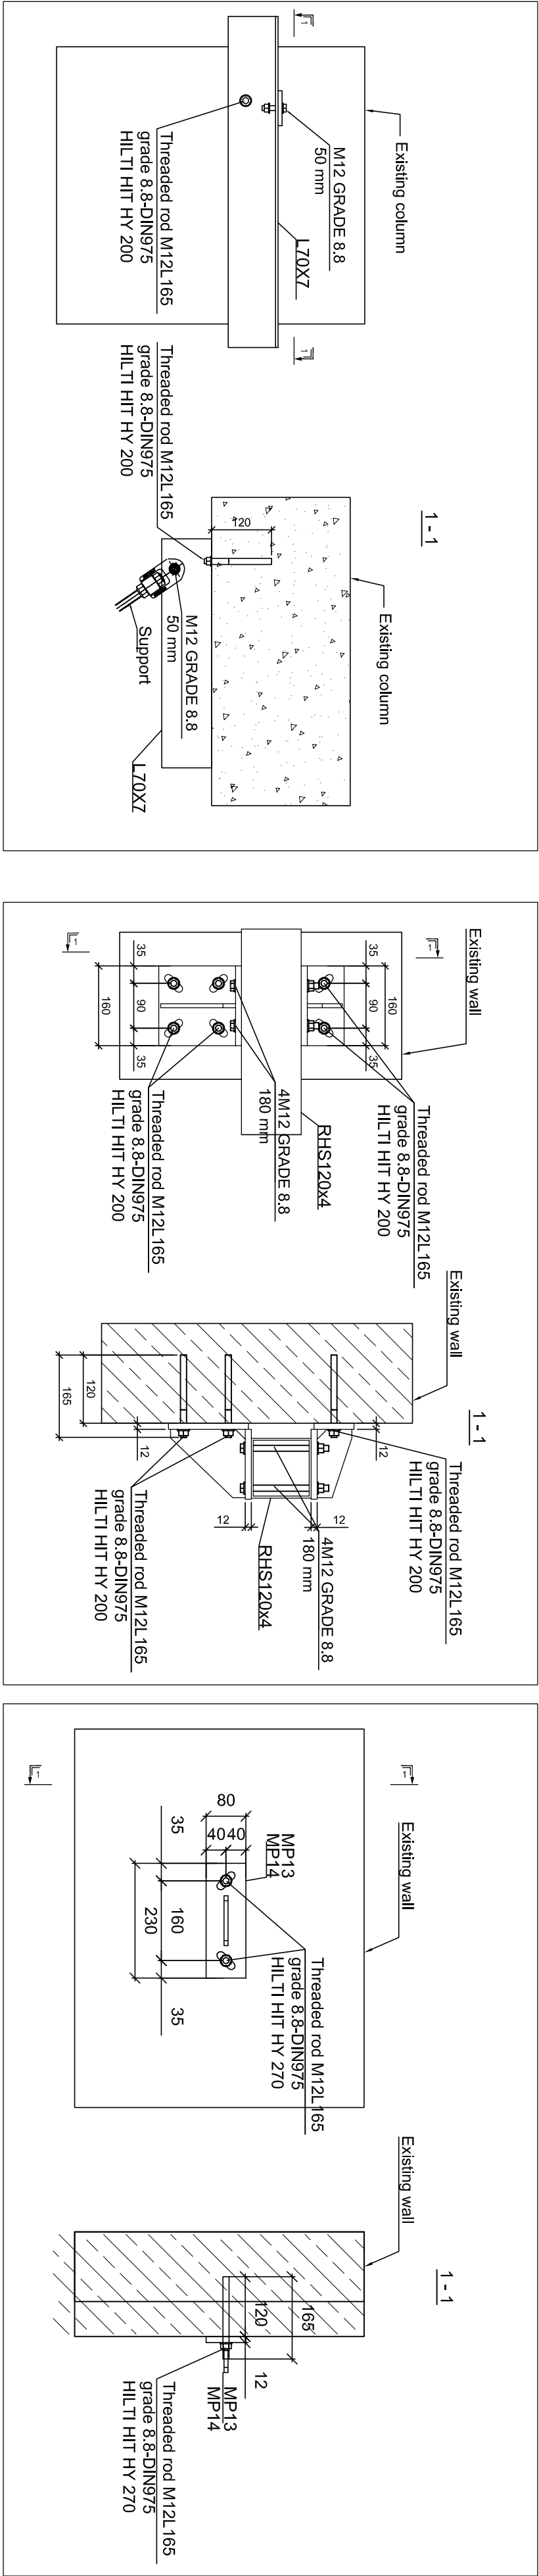

Steel column

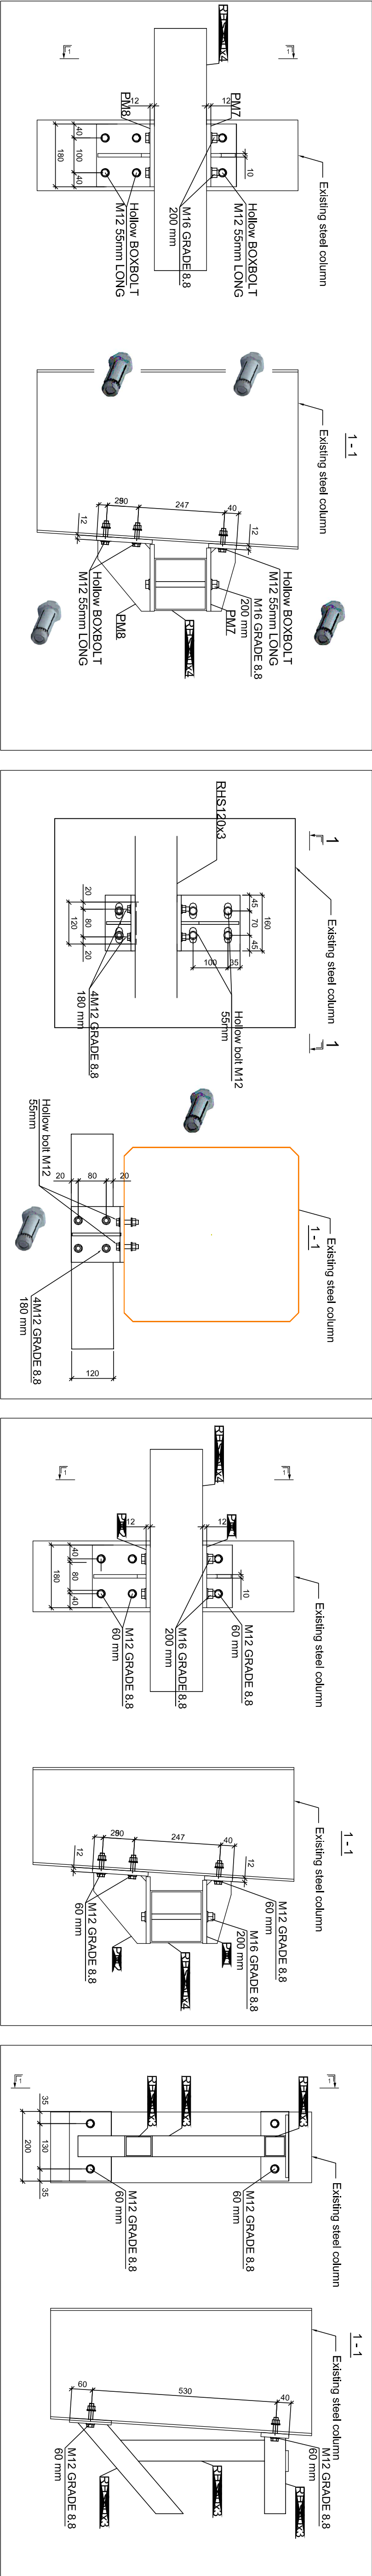

Masonry wall

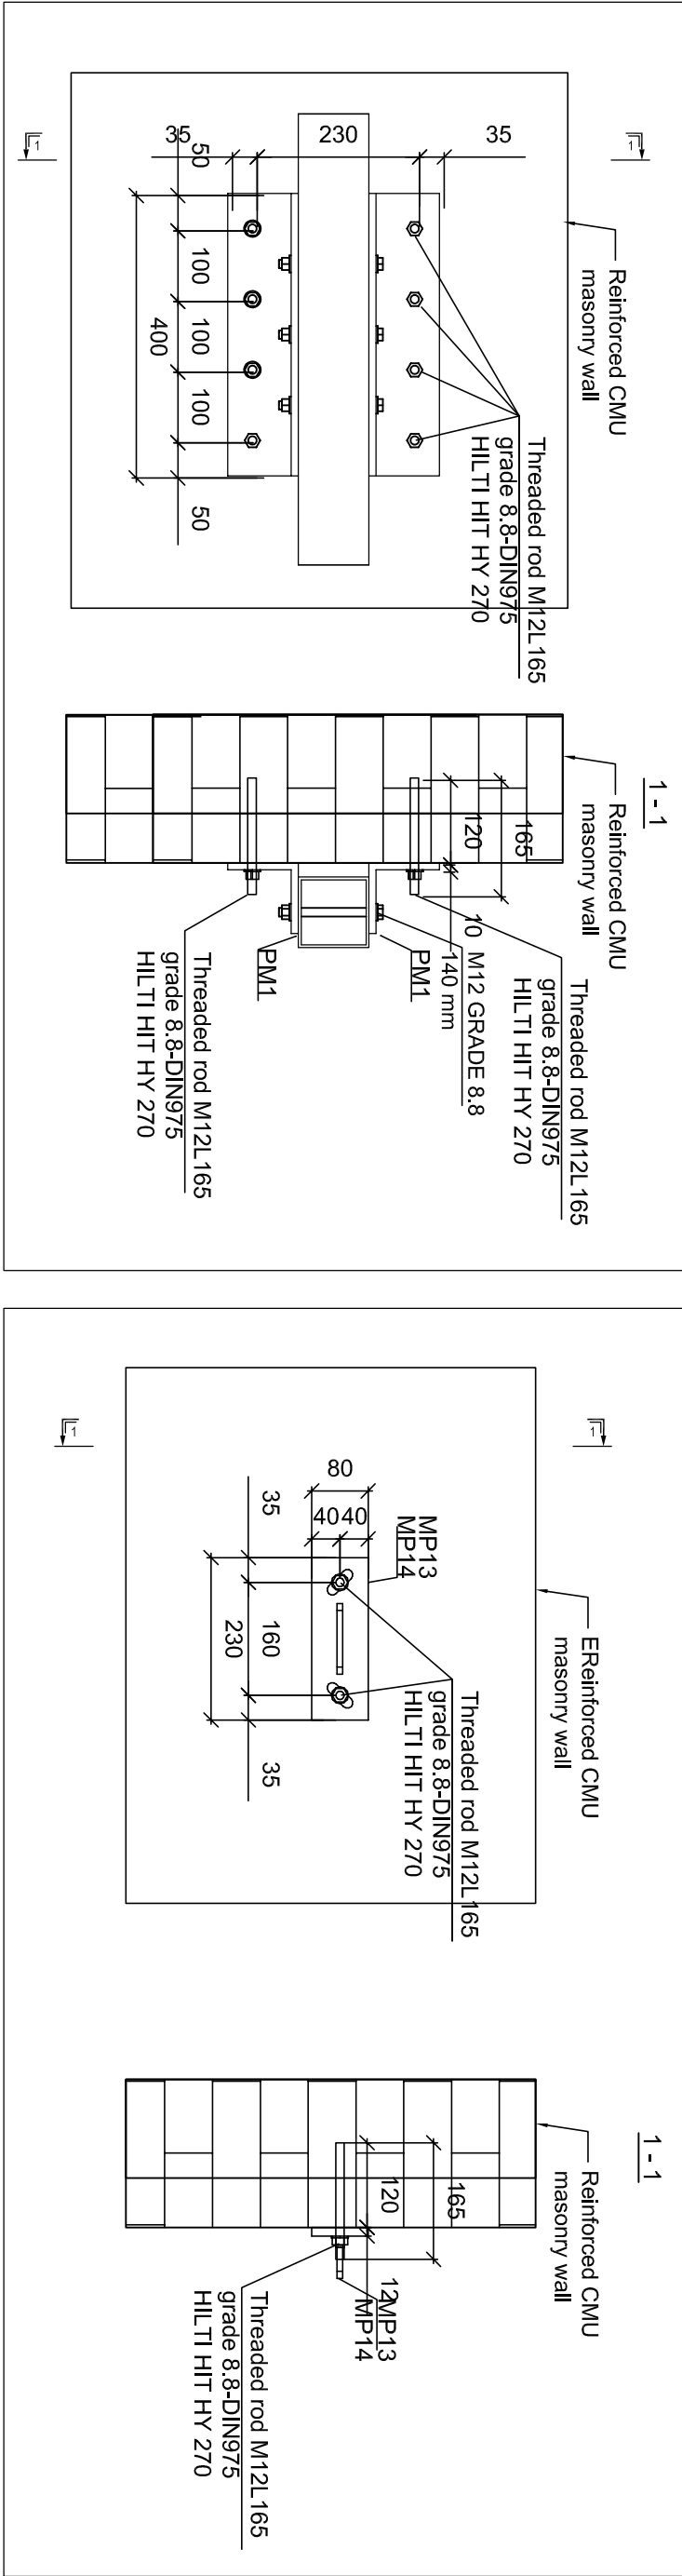

REVISIONS:	
No.	Date

All plans, engineering drawings, designs, images, trademarks and any other objects of IP are property of Valloppa AD and may not be used, duplicated, reproduced, modified, and/or distributed in any form without the explicit written consent of Valloppa AD.

CLIENT:

Country - City - Name

DRAWING INCLUDES: Details

DRAWN: ENG.B.Slovarov
CHECKED: ENG.P.PETROV
SCALE: 1:10 Format: A1
PROJECT NO.: T1-XXXX
SHEET: S10X
DRAWING: XX